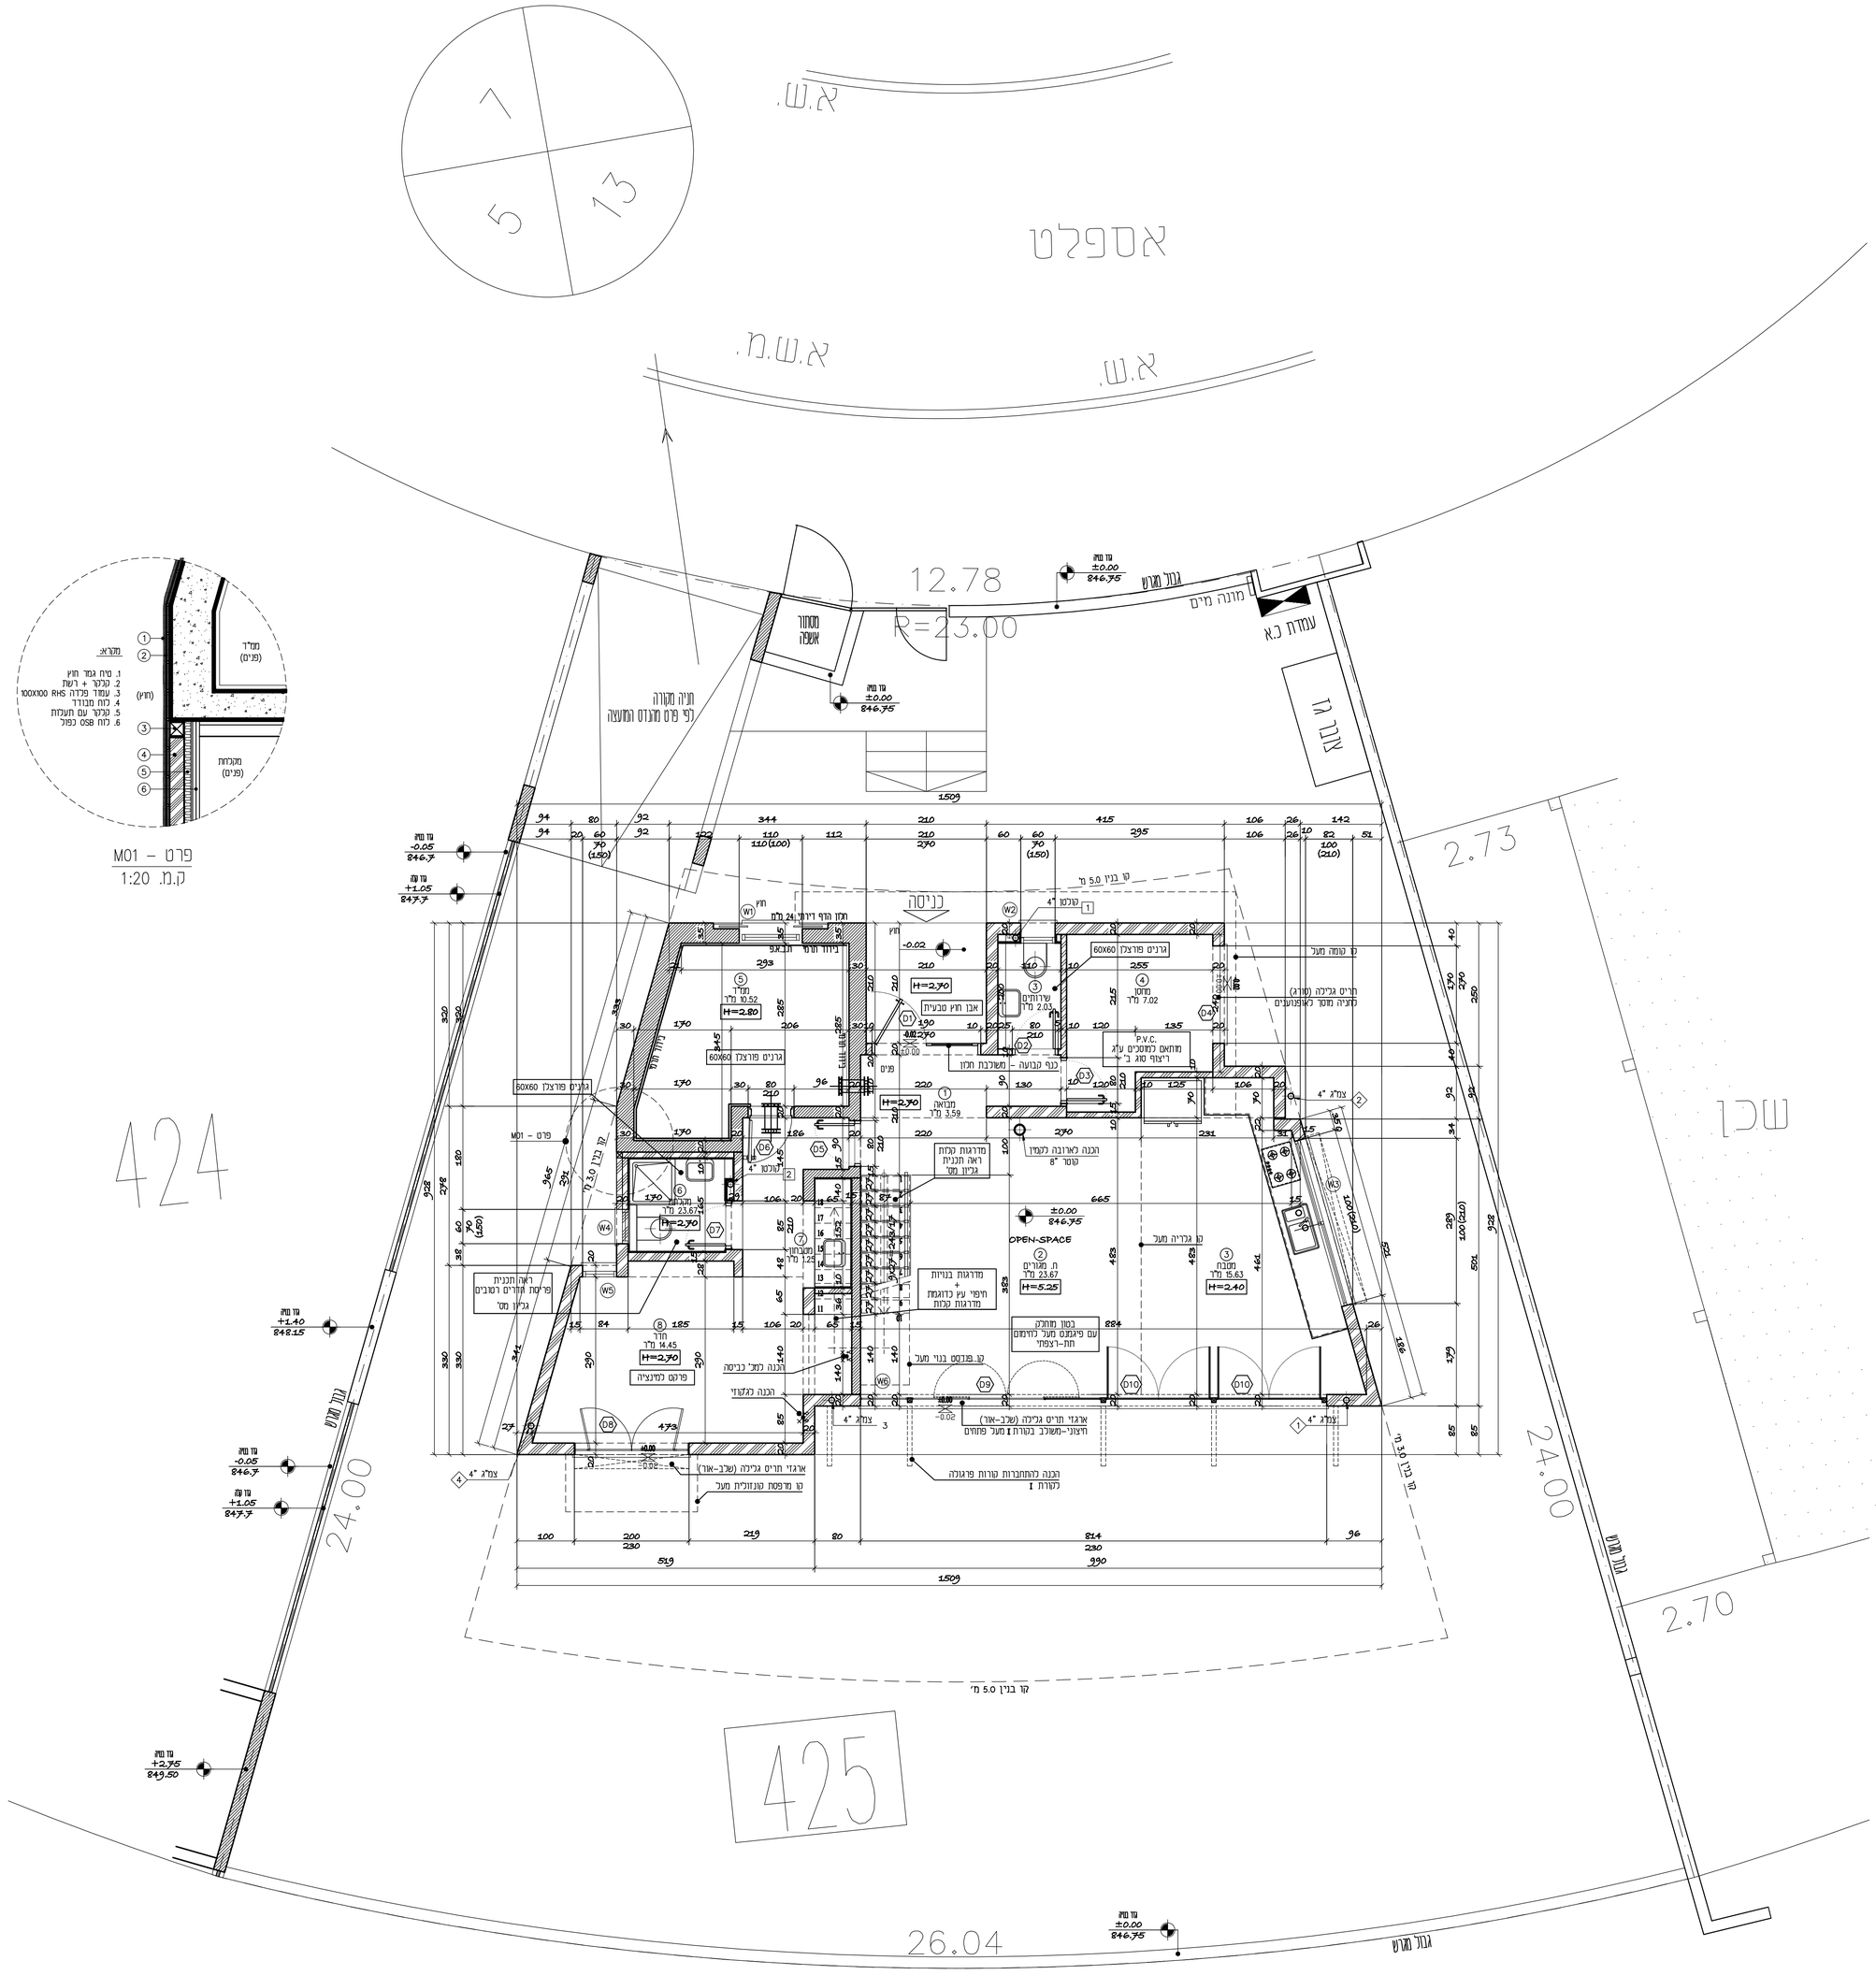
אספלט
א.ש.
א.ש.מ.
א.ש.
12.78
R=23.00
גבול מגרש
מונה מים
עמדת כ.א
עבר רגל
מחסן אשפה
תוי מקורה
לפי פרט מהנדס המועצה
כניסה
חדר מדרגות
חדר מכונות
מטבח
OPEN-SPACE
2.73
2.70
24.00
26.04
R=52.78
שכן
424
425
קו בנין 5.0 מ'
מדרגות קלות
ראה תכנית
פרטים חדרים רטובים
גרנים מס'
מדרגות בנויות
חיפוי עץ כדוגמת
מדרגות קלות
בטון מחוזק
עם פיגומים מעל לדיסים
תחת-רצפתי
הכנה לחלון כניסה
הכנה כלפשוי
פרקם למיגניה
אזורי תריס גגילה (שלב-אור)
חיצוני-משולב בקורות I מעל פתחים
הכנה להתחברות טורות פרגולה
לקורת I
קו מרפסת טונזוכית מעל
קו גגריה מעל
קו קומה מעל
תריס גגילה (שרג)
כלאיה מוסך לאופנועים
כנף קבועה - משולבת חלון
הכנה לארובה לכמין
קוטר "8
מדרגות קלות
ראה תכנית
גגיון מס'
מטבחון
מכבסה
חדר
מחסן
שרותים
אבן חוץ טבעית
גרנים פורצלן 60X60
P.V.C.
מותאם למוסכים ע"מ
ריצוף סוג ב'
מ"ד
מ"ד
מ"ד